


**PROPOSED PLAN OF G+VIII STORIED  
RESIDENTIAL BUILDING FOR TRIBHUVAN  
HOUSING CO-OPERATIVE SOCIETY LTD.  
AT PREMISES NO. 91-2222 (DC-204),  
NEW TOWN, RAJARHAT, KOLKATA**


ARCHITECTURAL DRAWING

**NOTES:-**


1. ALL DIMENSION ARE
2. ALL EXTERNAL WALLS  
75/125 mm. TH. AS
3. MIX OF CONCRETE
4. ALL REINFORCEMENT
5. THE DEPTH OF SEMI  
DEPTH OF NEIGHBOURING
6. a) ALL RECOMMENDATION  
TO THE PROJECT.
- b) TOP SLAB OF THE ULTRA  
STRUCTURALLY SAFE FOR
7. DOCUMENTS ENCLOSED  
a) N.O.C. OF WEST BENGAL  
b) N.O.C. OF CIVIL AVIATION  
c) N.O.C. of MICROWAVE

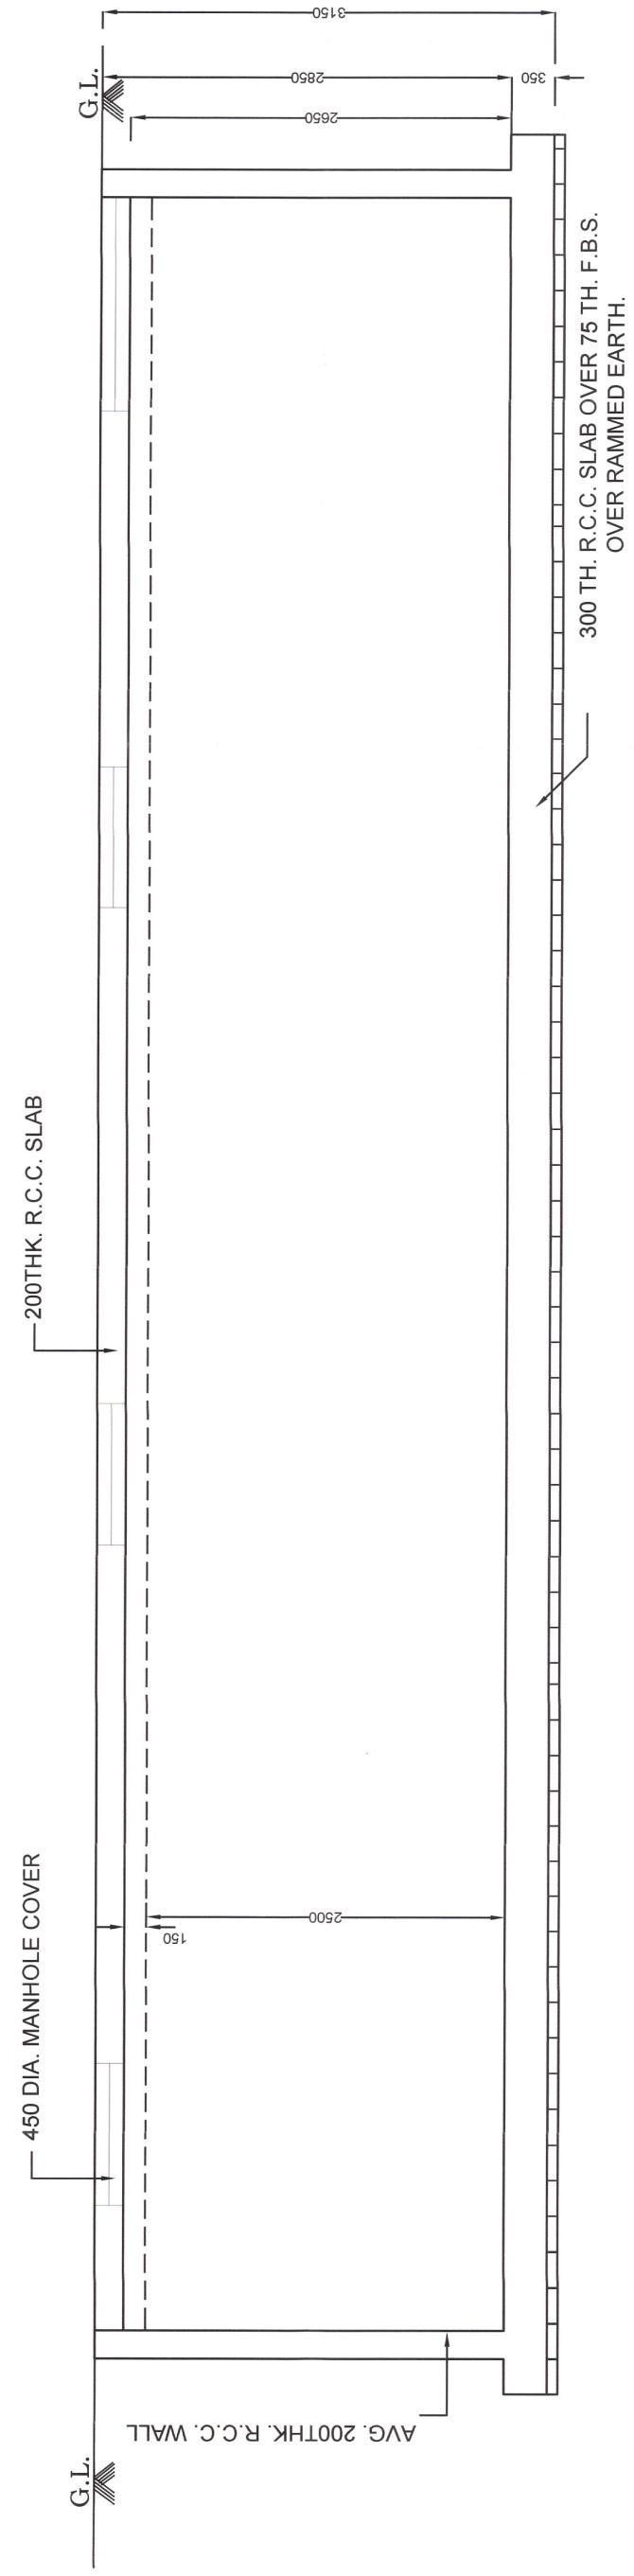


## SECTION THROUGH X-X

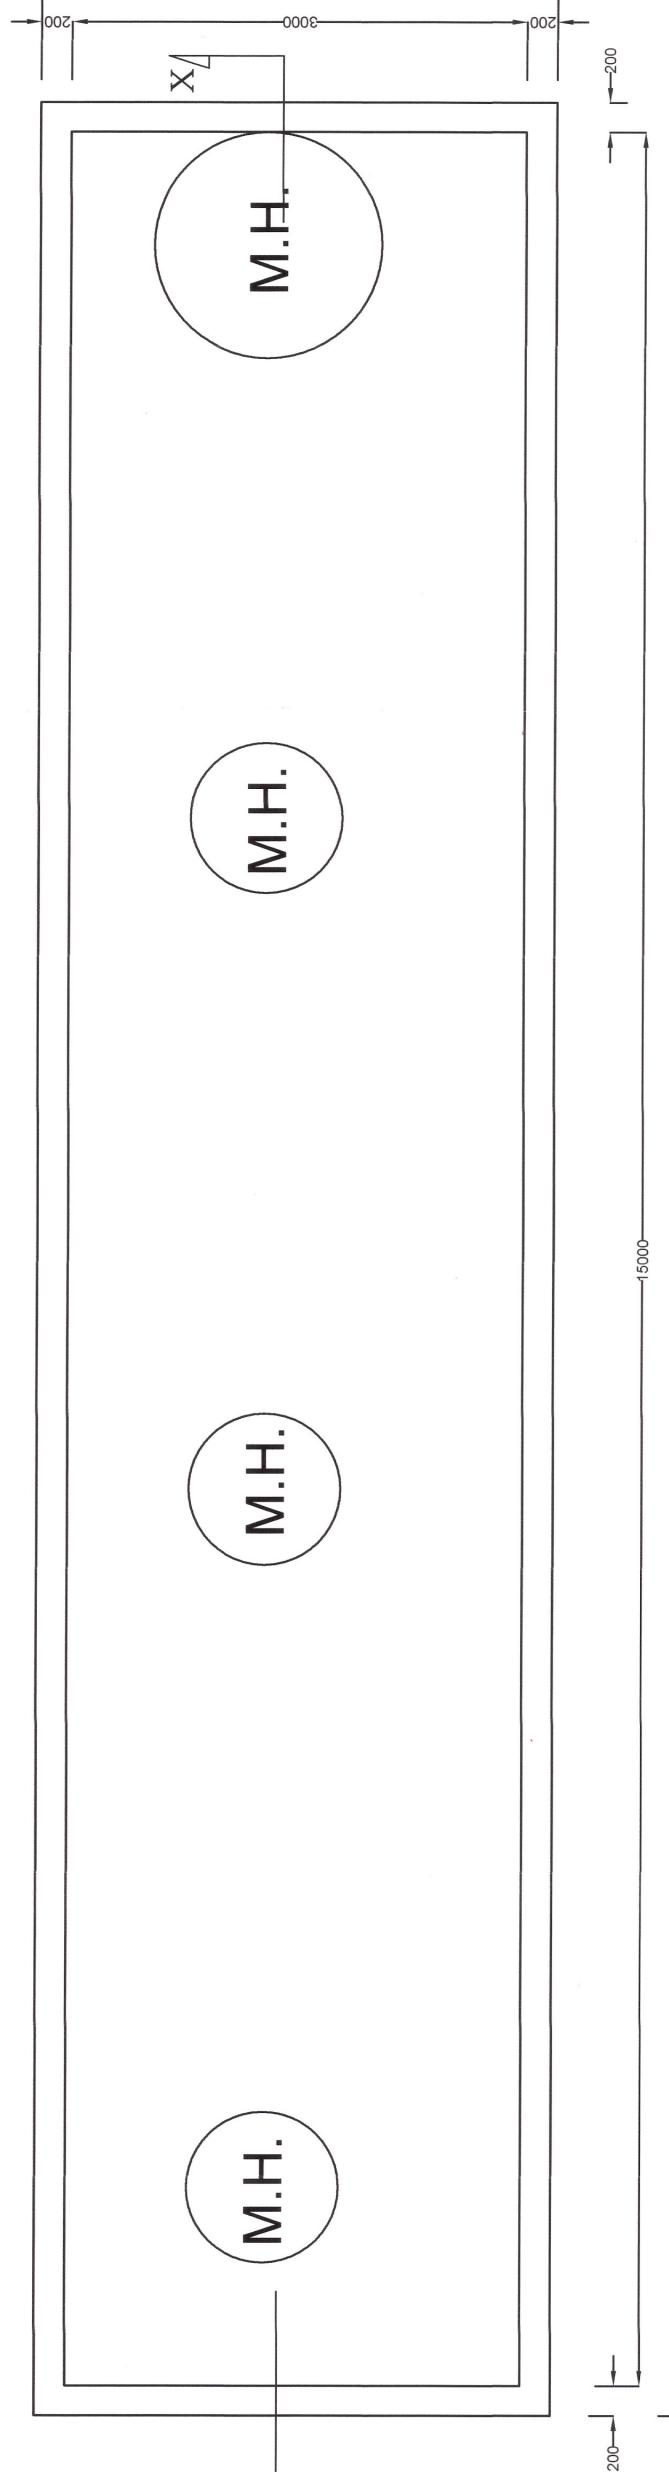


13400

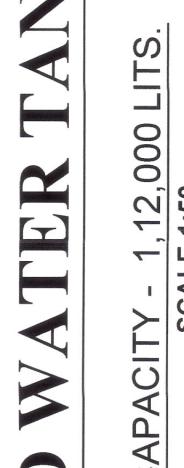


SCALE-1:50

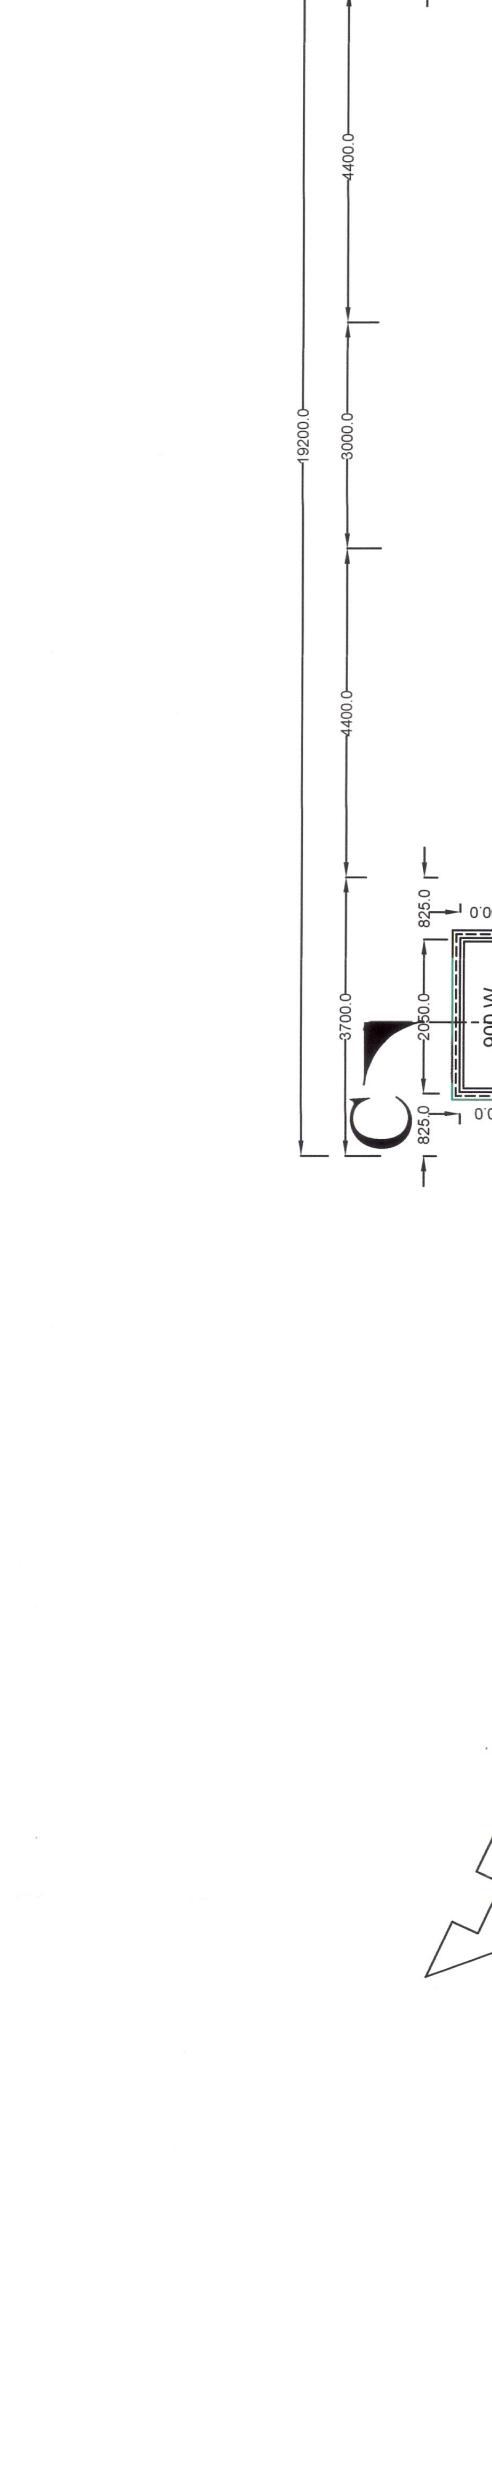


90% BALC

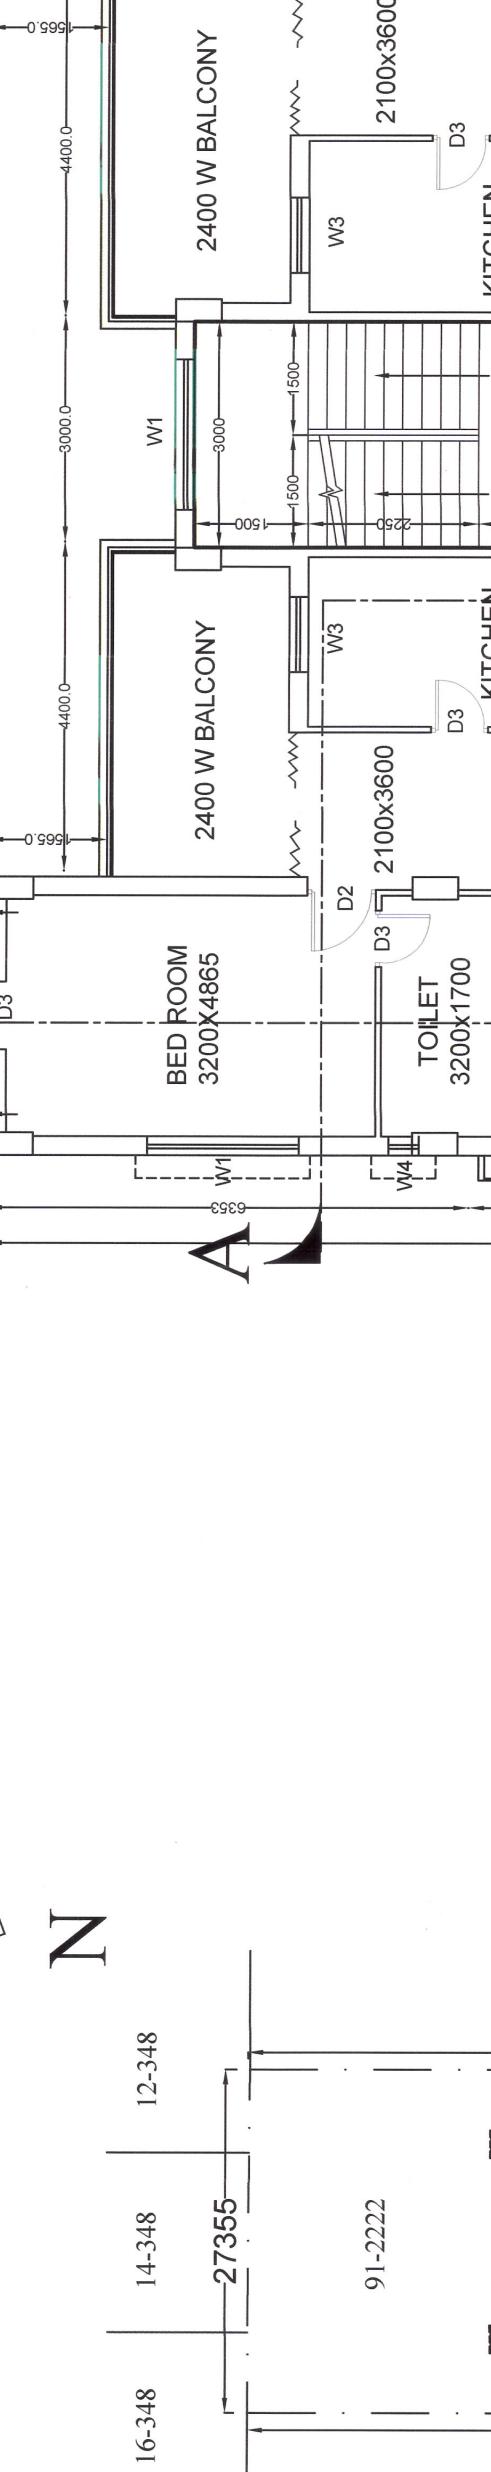


卷之三

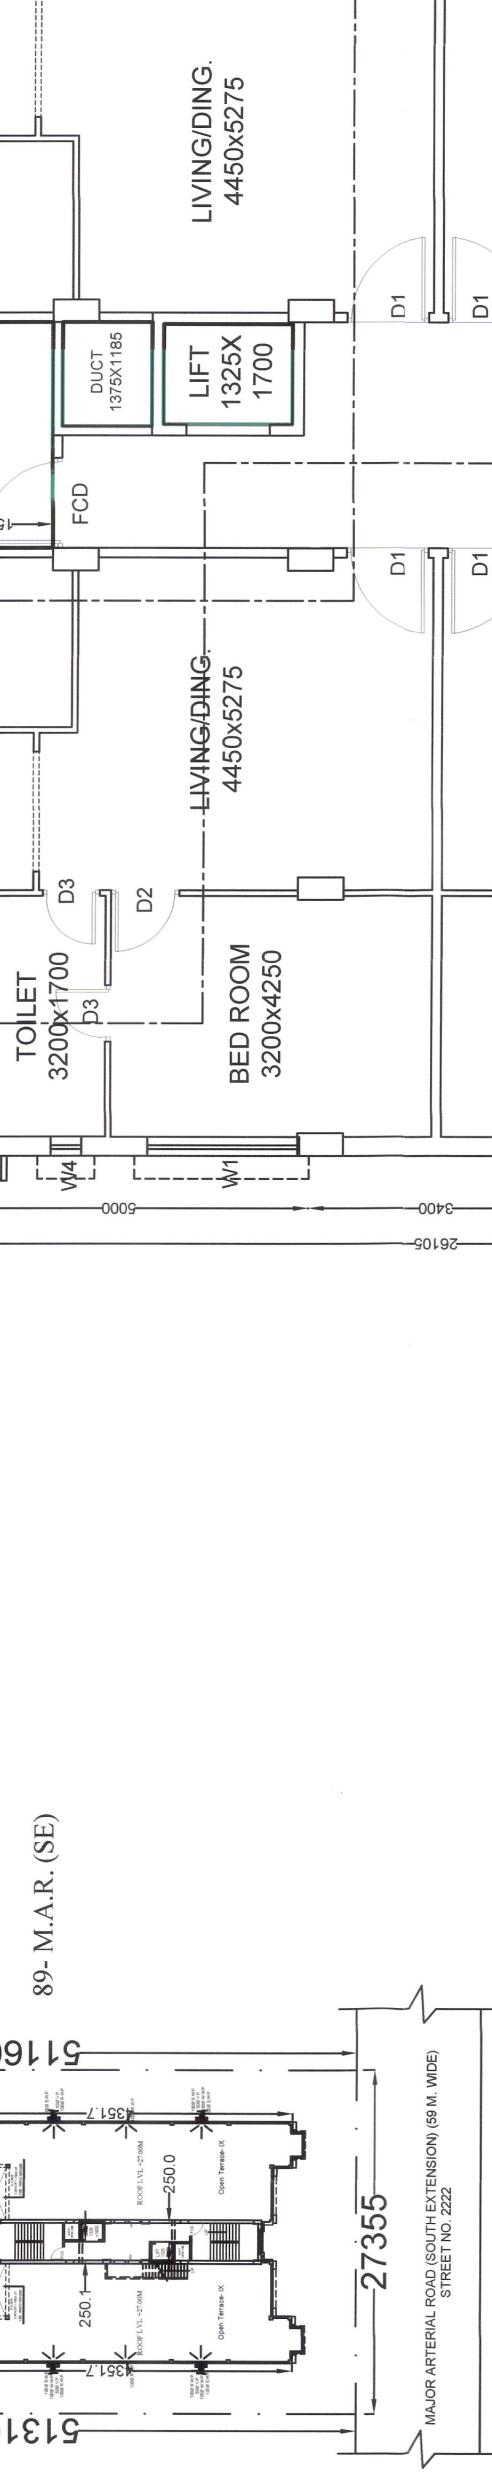

100

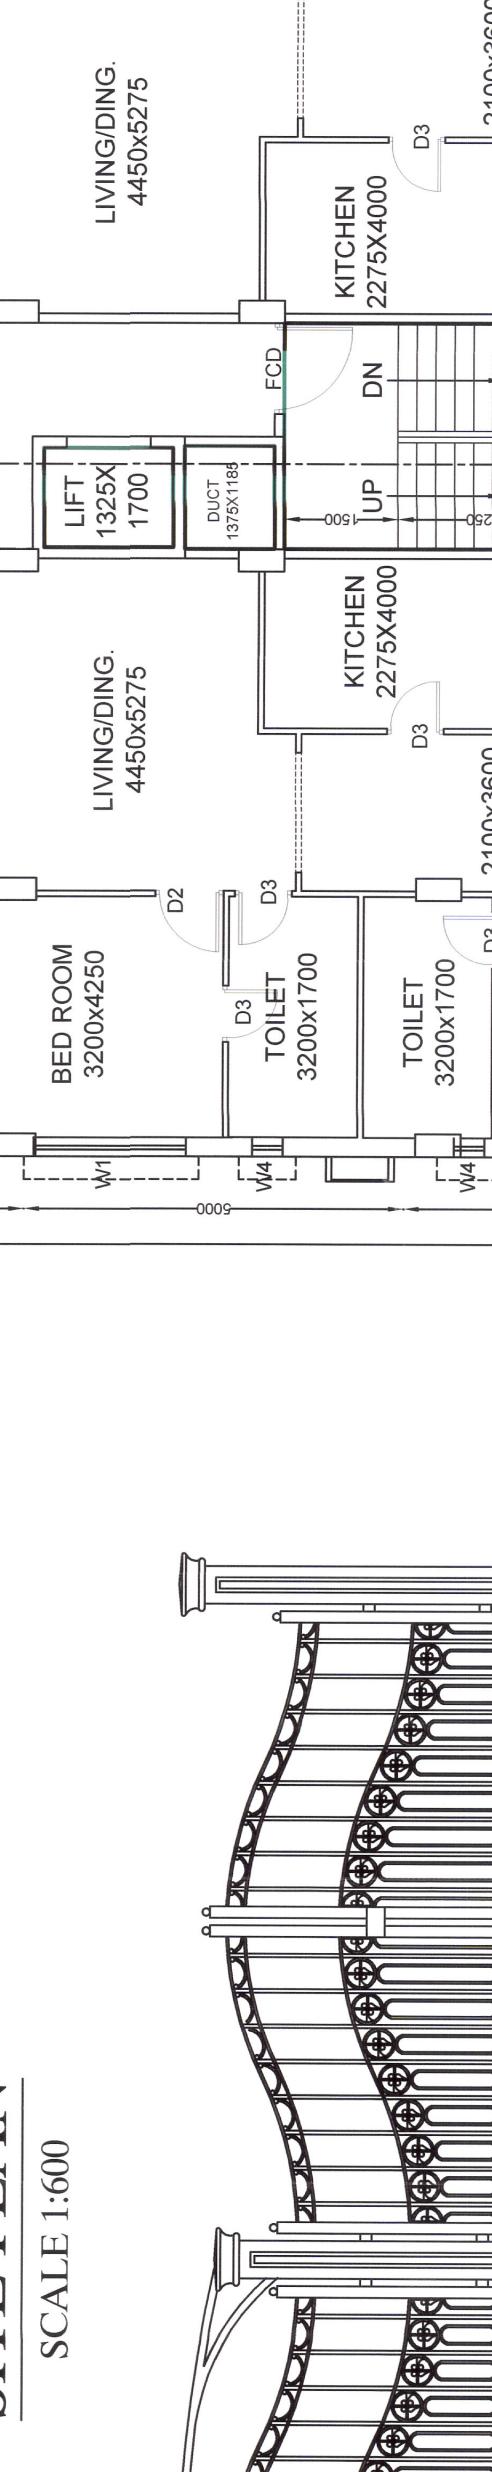


卷之三

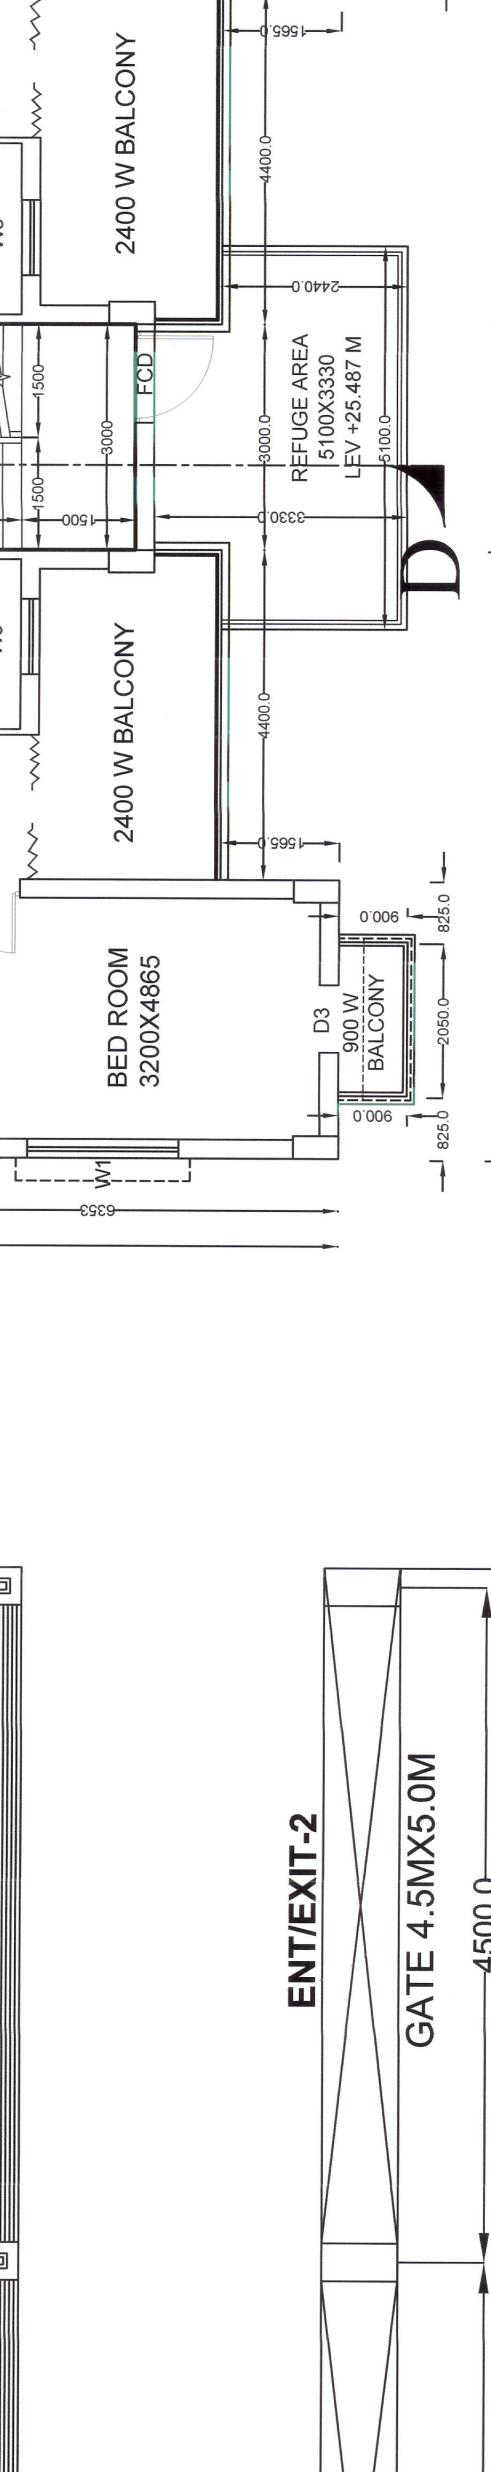

# 8TH. FLOOR PLAN



卷之三

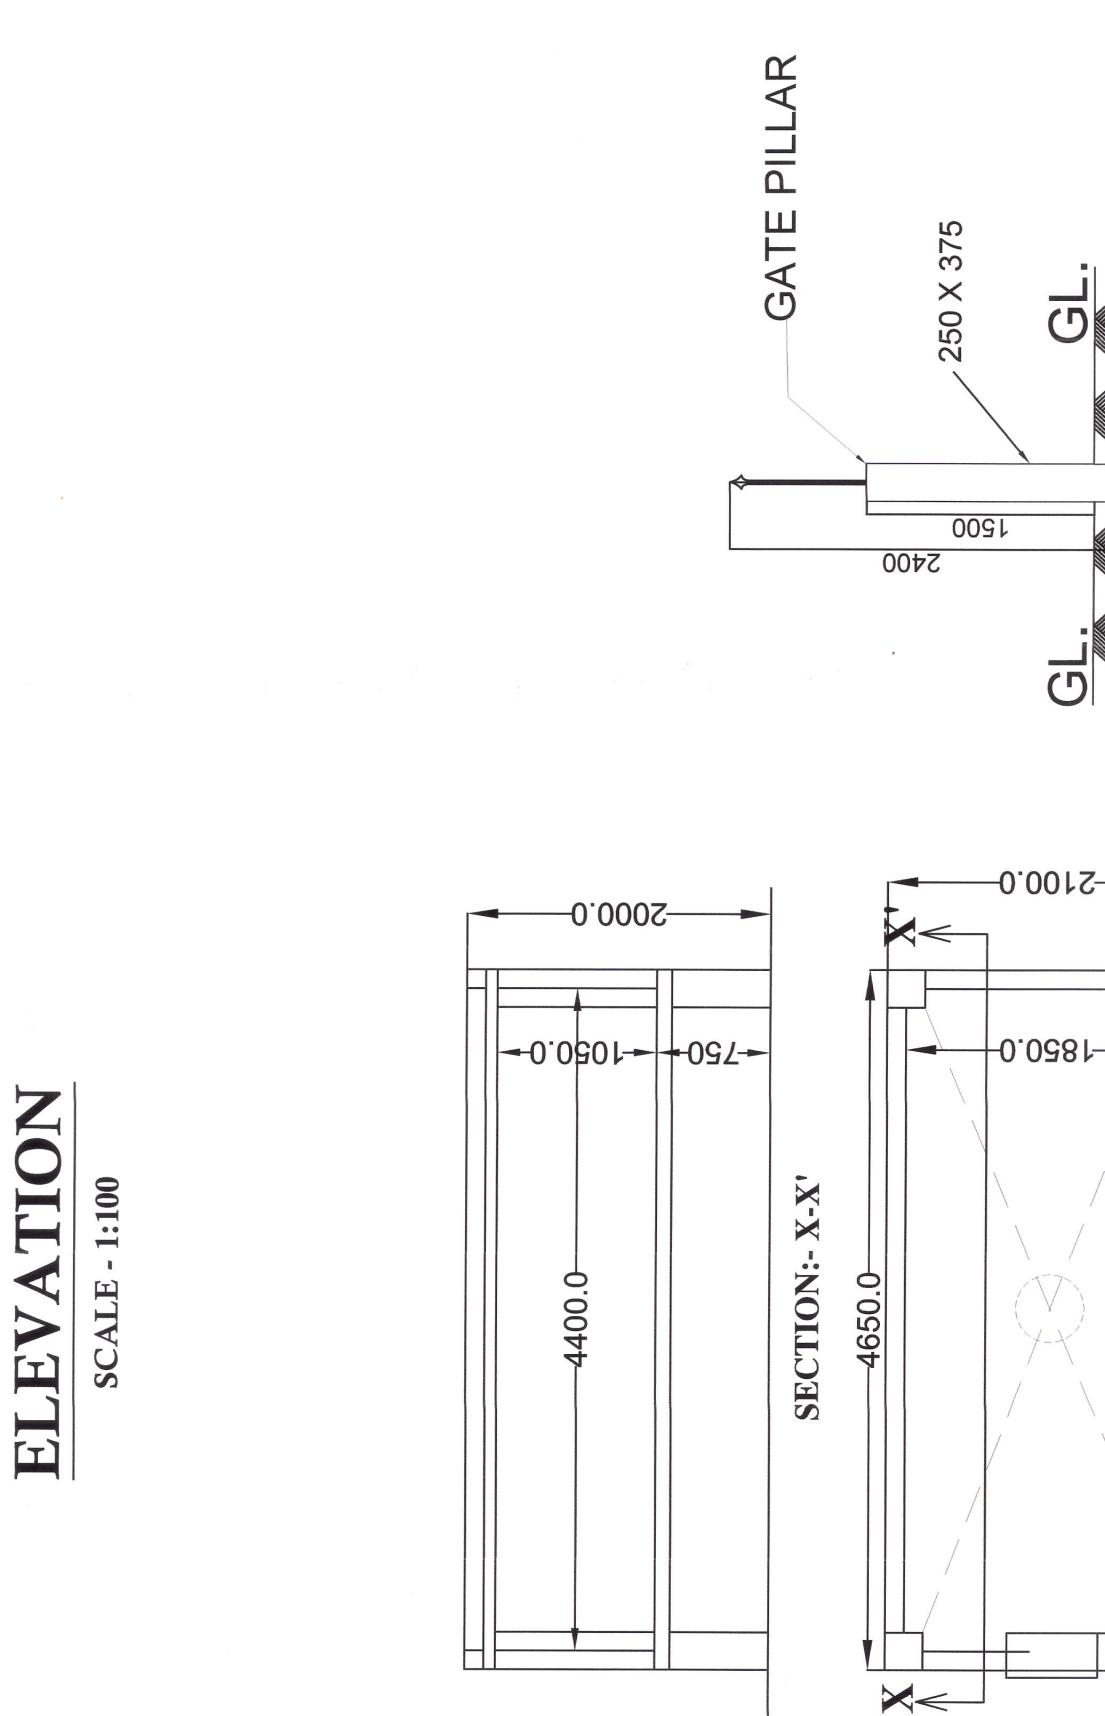

375 X 500

